



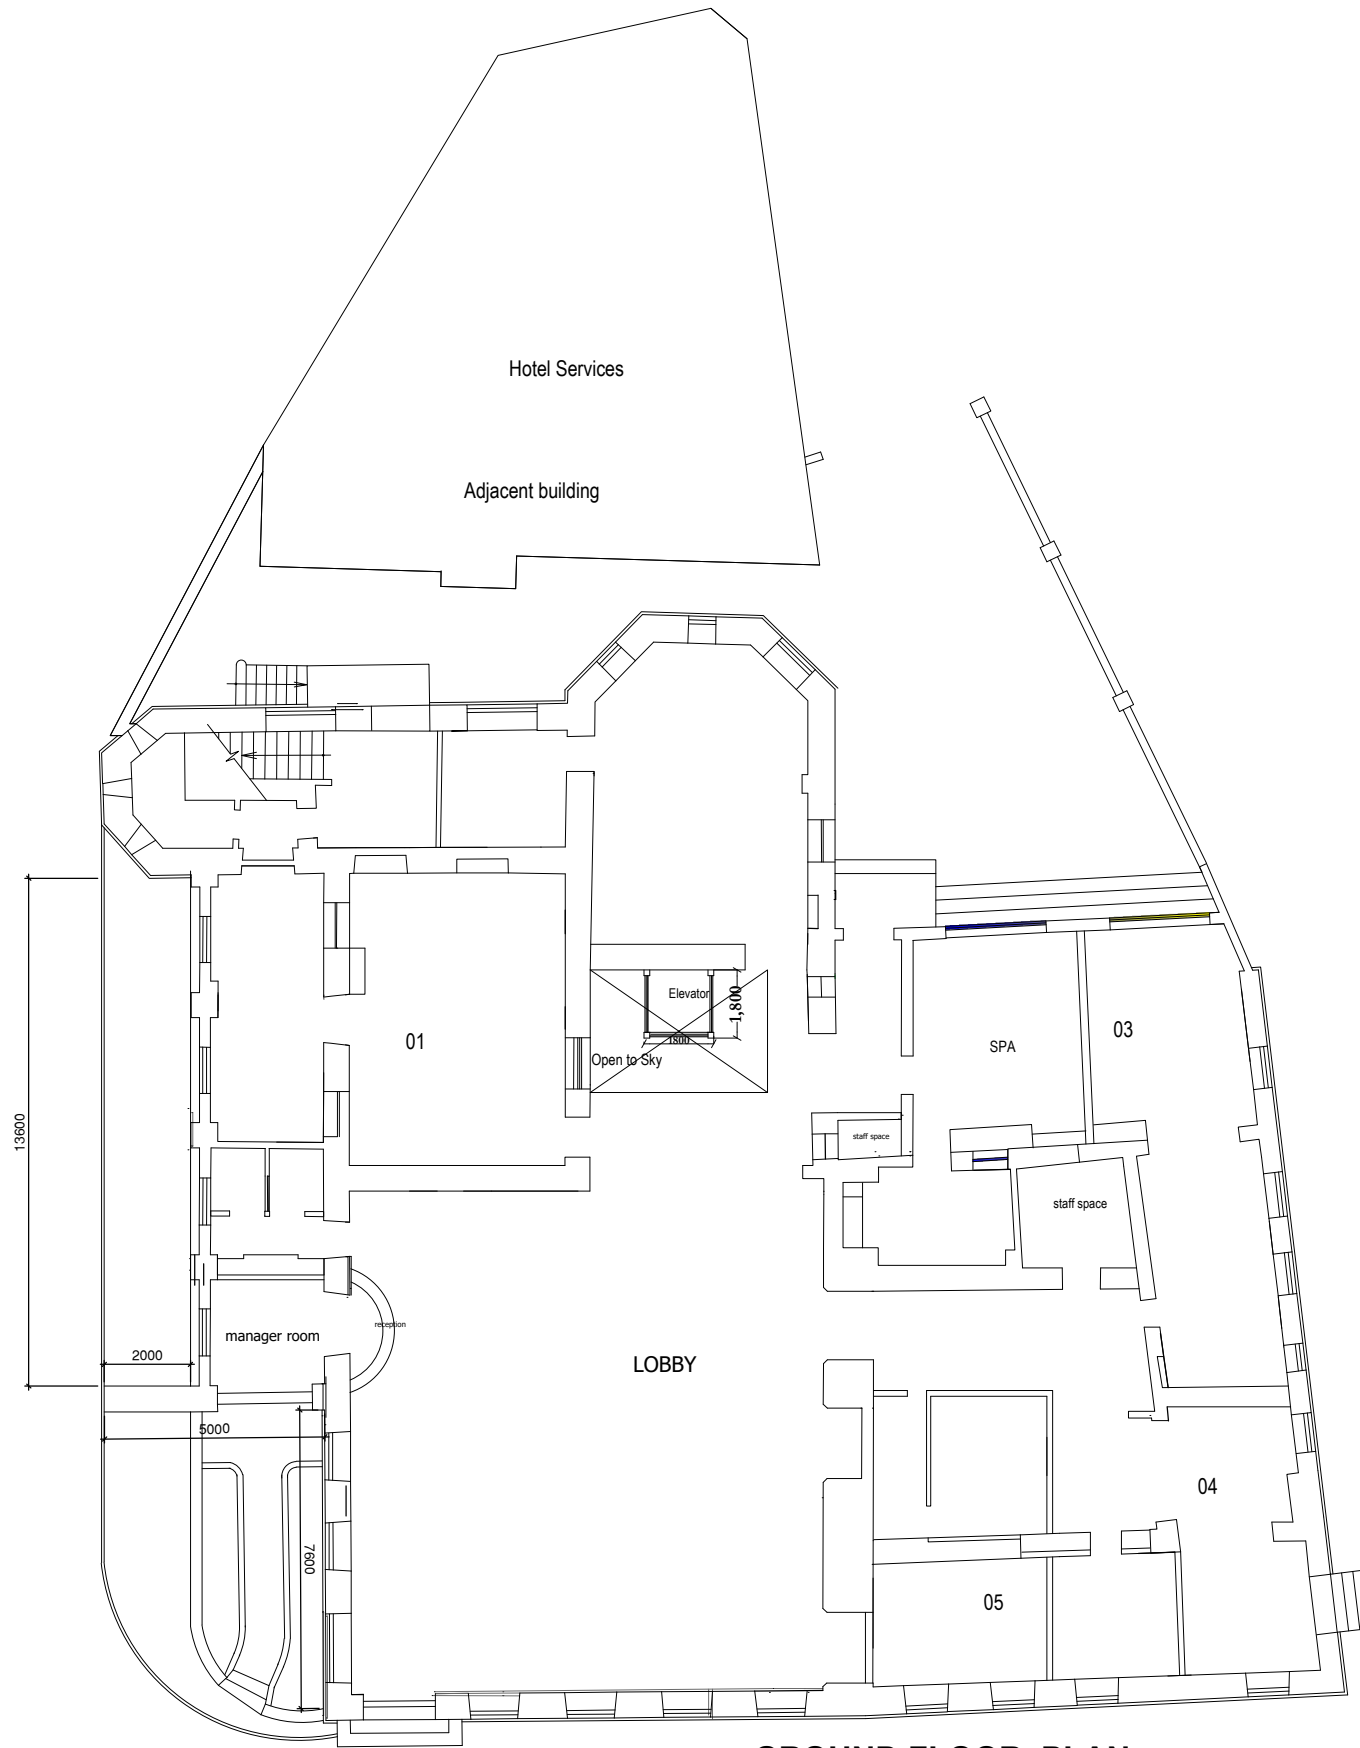

GROUND FLOOR PLAN

GENERAL NOTES:		
1. ALL DIMENSIONS ARE IN MM.		
2. READ THIS DRAWING IN CONJUNCTION WITH ARCHITECTURAL AND SERVICES DRAWINGS.		
4. REINFORCEMENTS SHALL BE :- MAIN BARS TYPE T, fy=460N/mm LINK BARS TYPE R, fy=250N/mm		
6. LAPS TO ALL REINFORCEMENTS SHALL BE 50 X BAR DIAMETER UNLESS OTHERWISE NOTED.		
7. COVER TO REINFORCEMENT SHALL BE - FOUNDATIONS 50MM - COLUMNS 30MM - BEAMS 25MM - SLAB 25MM - STAIRS 25MM		
8. DO NOT SCALE OUT THIS DRAWING		
rev.	date	
REVISIONS		
Discipline		
Project title and description		
Client		
Job stage and description		
Job No.		
Drawing Title :		
Drawing no.		Rev.
0		0
Designed by	Drawn by	Checked by
Approved By:	Date: MAY , 2026	Scale: AS SHOWN

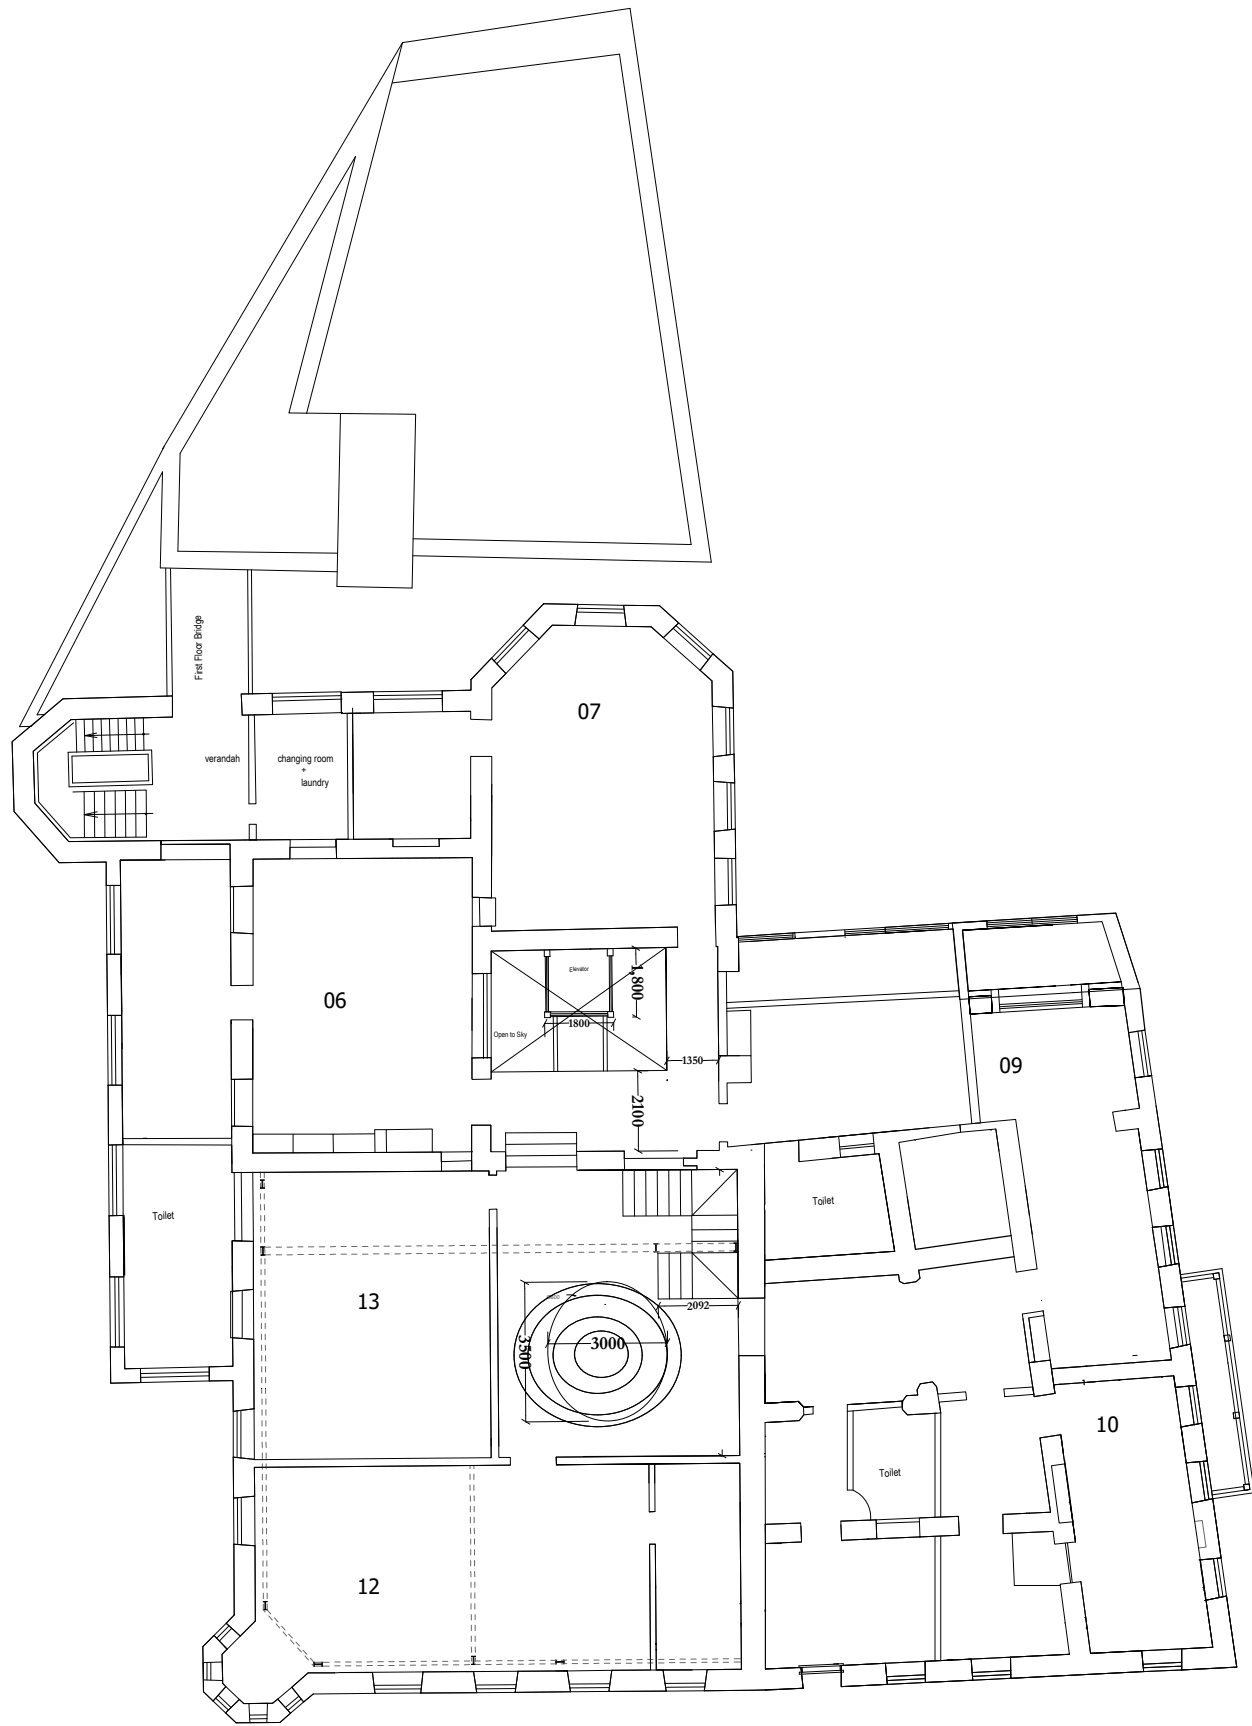


FIRST FLOOR PLAN

GENERAL NOTES:

1. ALL DIMENSIONS ARE IN MM.
2. READ THIS DRAWING IN CONJUNCTION WITH ARCHITECTURAL AND SERVICES DRAWINGS.
4. REINFORCEMENTS SHALL BE :-
MAIN BARS TYPE T, $f_y=460\text{N/mm}$
LINK BARS TYPE R, $f_y=250\text{N/mm}$
6. LAPS TO ALL REINFORCEMENTS SHALL BE 50 X BAR DIAMETER UNLESS OTHERWISE NOTED.
7. COVER TO REINFORCEMENT SHALL BE
- FOUNDATIONS 50MM
- COLUMNS 30MM
- BEAMS 25MM
- SLAB 25MM
- STAIRS 25MM
8. DO NOT SCALE OUT THIS DRAWING

rev.	date	
REVISIONS		
Discipline		
Project title and description		
Client		
Job stage and description		
Job No.		
Drawing Tittle :		
Drawing no.		Rev.
0		0
Designed by	Drawn by	Checked by
Approved By:	Date: MAY, 2026	Scale: AS SHOWN

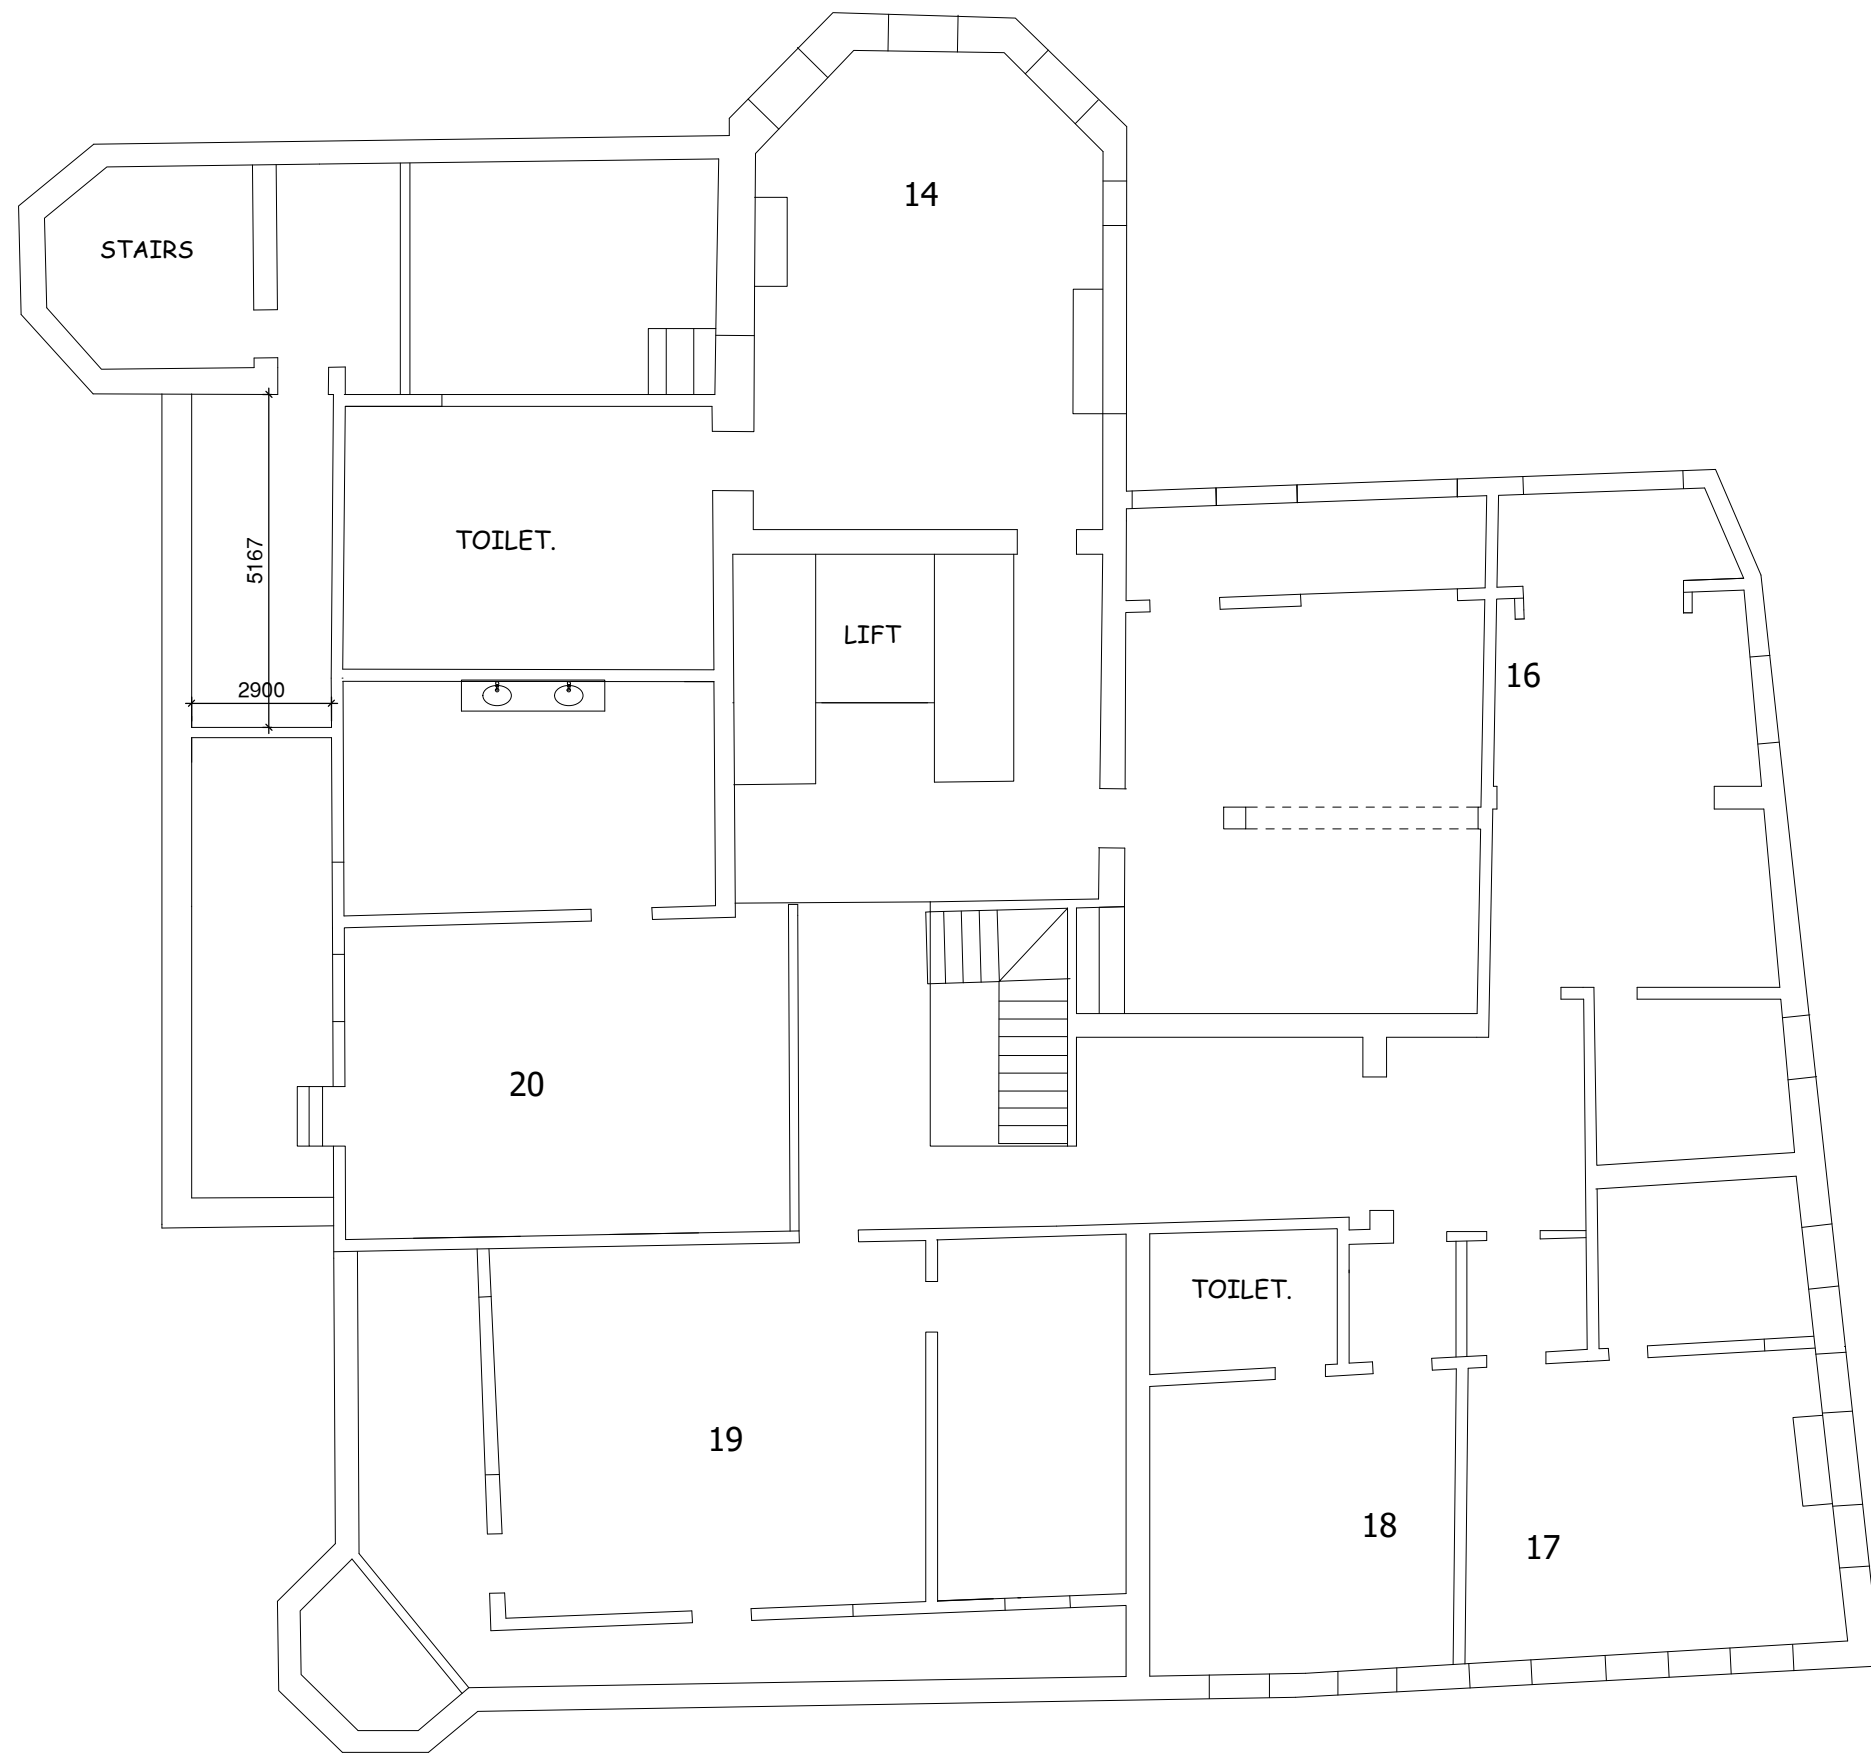

SECOND FLOOR PLAN

GENERAL NOTES:

- 1. ALL DIMENSIONS ARE IN MM.
- 2. READ THIS DRAWING IN CONJUNCTION WITH ARCHITECTURAL AND SERVICES DRAWINGS.
- 4. REINFORCEMENTS SHALL BE :-
MAIN BARS TYPE T, $f_y=460\text{N/mm}$
LINK BARS TYPE R, $f_y=250\text{N/mm}$
- 6. LAPS TO ALL REINFORCEMENTS SHALL BE 50 X BAR DIAMETER UNLESS OTHERWISE NOTED.
- 7. COVER TO REINFORCEMENT SHALL BE
 - FOUNDATIONS 50MM
 - COLUMNS 30MM
 - BEAMS 25MM
 - SLAB 25MM
 - STAIRS 25MM
- 8. DO NOT SCALE OUT THIS DRAWING

rev.	date	
REVISIONS		
Discipline		
Project title and description		
Client		
Job stage and description		
Job No.		
Drawing Title :		
Drawing no.		Rev.
0		0
Designed by	Drawn by	Checked by
Approved By:	Date: MAY, 2026	Scale: AS SHOWN